
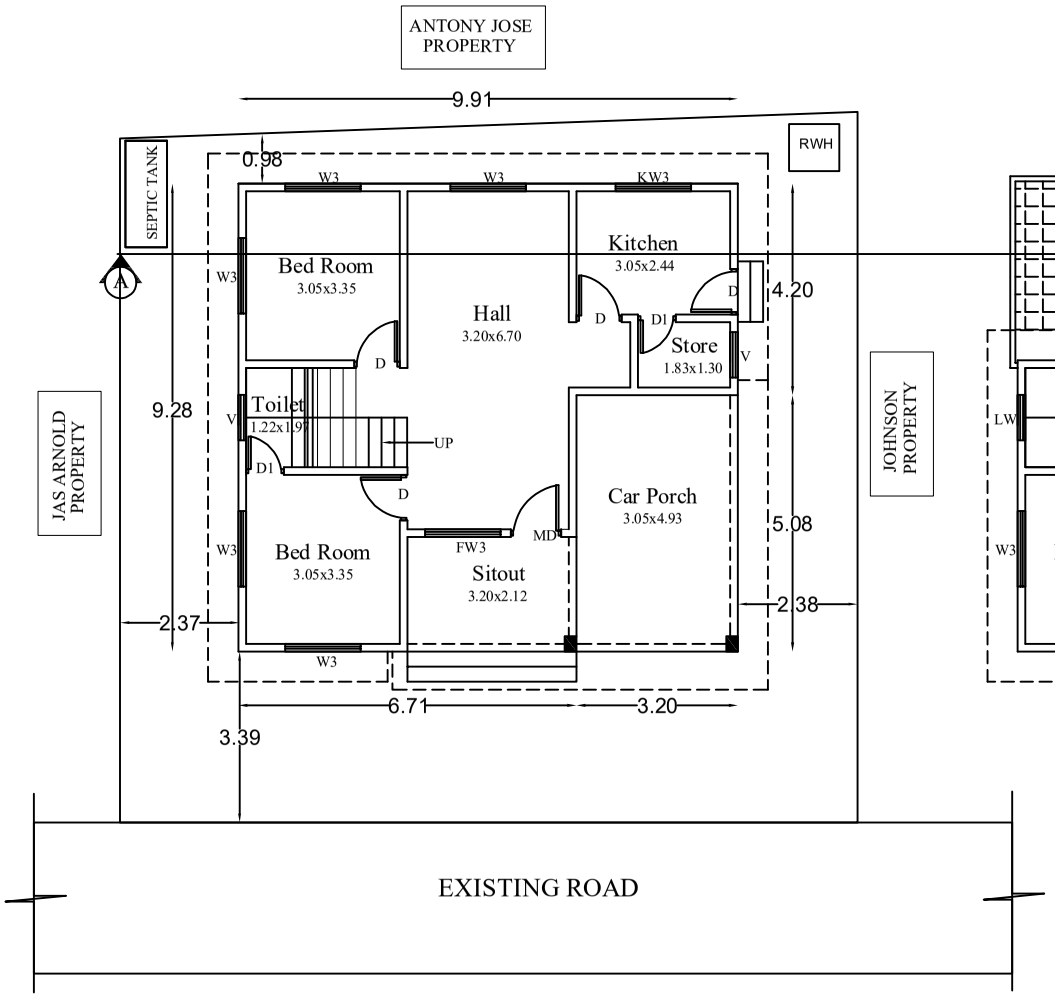


SITE CUM GROUND FLOOR PLAN

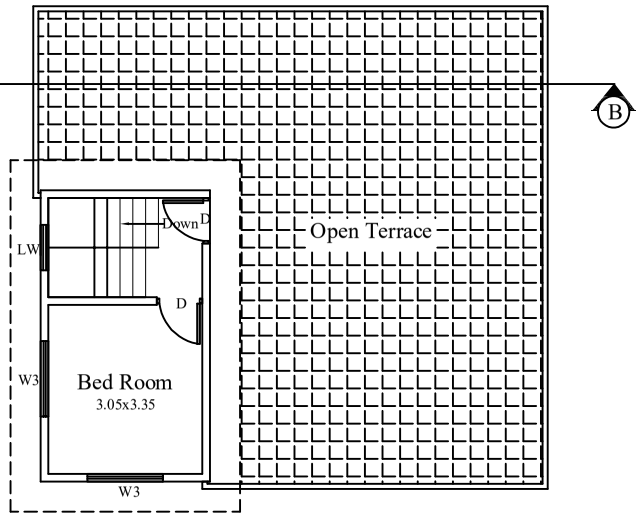

FIRST FLOOR PLAN

SHEET NO: 01 / 02

PLAN SHOWING THE PROPOSED CONSTRUCTION OF RCC ROOF RESIDENTIAL BUILDING IN RE.SY.NO: 722/12A1 AT CITTATTUVILAI, KUZHICODE, KUZHICODE POST WITH IN MARUTHOORKURICHY VILLAGE, MULAGUMOODU TOWN PANCHAYAT, KALKULAM TALUK, K.K.DIST.

NOTE : ALL DIMENSIONS ARE IN METRE

AREA STATEMENT DETAILS

SITE AREA : 202.40 SQ.M (2178.63 SQ.FT)

PROPOSED RESIDENTIAL BUILDING AREA DETAILS :

S.NO	DESCRIPTION	FSI (SQ.M)	NON-FSI (SQ.M)	TOTAL (SQ.M)
01	GROUND FLOOR	91.96	-	91.96
	FIRST FLOOR	19.38	-	19.38
	TERRACE FLOOR	-	-	-
	TOTAL AREA	111.34	-	111.34

TOTAL FSI AREA = 111.34 SQ.M

FLOOR SPACE INDEX = $\frac{111.34}{202.40}$ = 0.550

JOINERY SCHEDULE

DOOR	MD : 1.00 x 2.10
DOOR	D : 0.90 x 2.10
DOOR	D1 : 0.76 x 2.10
WINDOW	LW : 0.90 x 1.80
WINDOW	W3 : 1.50 x 1.50
WINDOW	KW3 : 1.50 x 1.00
VENTILATION	V : 0.90 x 0.60

INDEX :

EX.ROAD

BOUNDARY

PROPOSED BUILDING

EXISTING BUILDING

REFERENCE :

SCALE : 1:100

DATE : 19/08/2024

ARCHITECT / REGISTERED ENGINEER :

Mr.P. YESU RAJ ,
S/O. Mr. PANKIRAJ,
CITTATTUVILAI,
KUZHICODE,
KUZHICODE POST,
K.K.DIST. PIN:629167.

ADDRESS & SIGNATURE OF THE OWNER

DWELLING UNITS DETAILS :

DWELLING UNITS : 01	111.34 SQ.M